


TOPOGRAPHICAL SURVEY MAP OF PARCEL NUMBER 5830-016-057 (0.53 Acs)

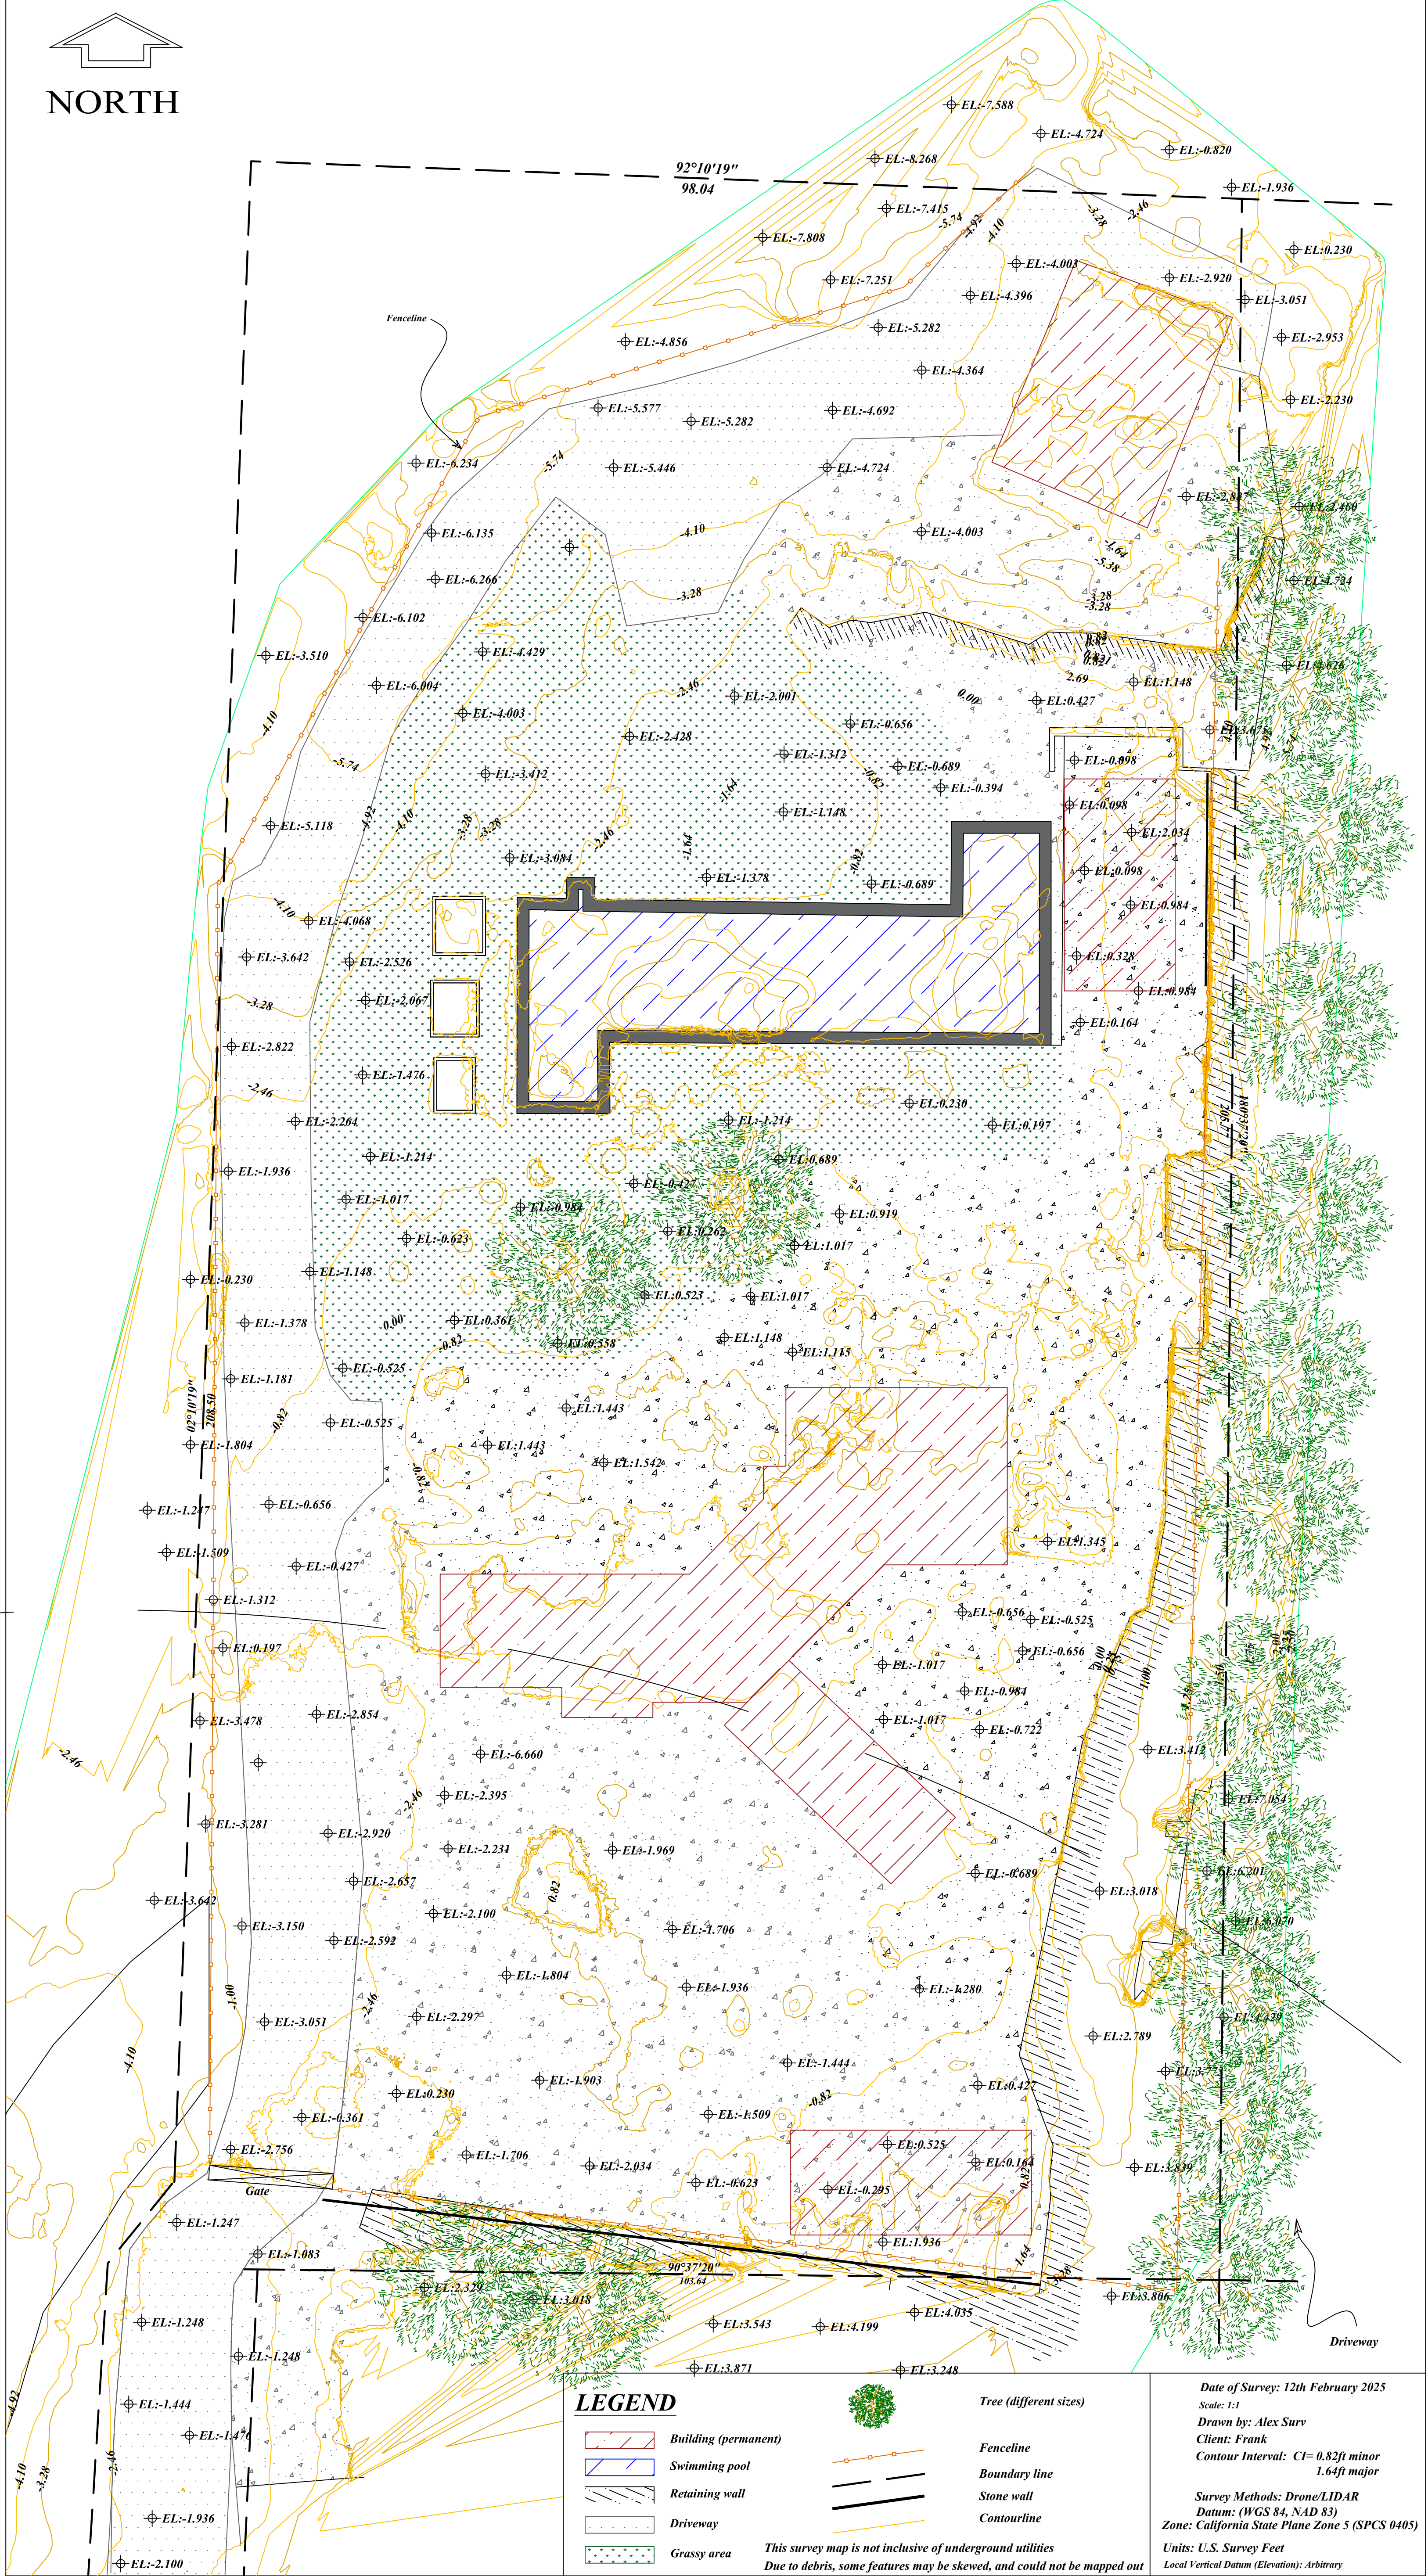

LEGEND


- Building (permanent)
- Swimming pool
- Retaining wall
- Driveway
- Grassy area



Tree (different sizes)




Fence line

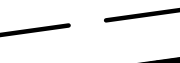

Boundary line



Stone wall

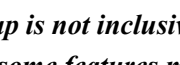

Contour line

This survey map is not inclusive of underground utilities
Due to debris, some features may be skewed, and could not be mapped out

Date of Survey: 12th February 2025

Scale: 1:1

Drawn by: Alex Surv

Client: Frank

Contour Interval: CI= 0.82ft minor
1.64ft major

Survey Methods: Drone/LIDAR

Datum: (WGS 84, NAD 83)

Zone: California State Plane Zone 5 (SPCS 0405)

Units: U.S. Survey Feet

Local Vertical Datum (Elevation): Arbitrary